
STEP2　プランター台をつくる

材料費 **約500円**　　作業時間 **半日**　　材料 **STEP1の余り＋2×4材1本**

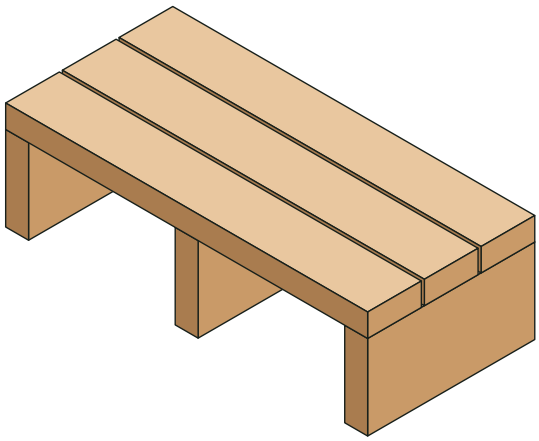

完成図（幅600×奥行き277×高さ178mm）

STEP1
踏み台
切る・留める

STEP2
プランター台
板を張る

STEP3
囲炉裏テーブル
枠を組む

STEP4
木製門扉
柱を建てる

卒業制作
ウッドデッキ
すべてを使う

STEP2で覚えること

1. **板を支える「根太」を、等しい間隔で並べる**
   根太の間隔は、板がたわまない長さにする
2. **すき間をそろえて、板を張る**
   5mmの「すき間ゲージ」をはさむだけでそろう
3. **ビスの位置を、一直線にそろえる**
   先に線を引いてから打つと、見た目がぐっと良くなる
4. **板の幅とすき間から、全体の寸法を決める（割付け）**
   板3枚＋すき間2つ＝277mm

> **ウッドデッキでは：**プランター台は、ウッドデッキを小さく切り取ったものです。根太の上に床板を張る作り方は、デッキとまったく同じです。

道具と材料

買ったらチェック

材料（約500円）

材料	規格	数量	目安
☐ 2×6材（STEP1の余り）	38×140mm　長さ約914mm	1本	—
☐ 2×4材	38×89mm　長さ1,820mm	1本	￥500
☐ コーススレッド 75mm（STEP1の残り）	使うのは18本	—	—
☐ すき間ゲージ	厚さ5mmの端材（ベニヤ板など）2枚	2枚	—
☐ 塗料（あれば）	屋外用の木材保護塗料	—	—
合計（目安）			**￥500**

STEP1から始めていない場合は、2×6材1,820mmを1本（約900円）とコーススレッド75mm（約500円）を追加。鉢を置くので、屋外用の塗料を塗っておくと長持ちする。

道具（STEP1と同じ）

- ☐ さしがね・メジャー・鉛筆
- ☐ ノコギリ（または丸ノコ）
- ☐ インパクトドライバー・下穴用ドリル 3mm
- ☐ サンドペーパー #120
- ☐ 保護メガネ・手袋

STEP2で新しく使うもの

- ☐ まっすぐな長い定規（なければ2×4材の端材）
- ☐ すき間ゲージ（上の材料表）

割付け（わりつけ）の考え方

奥行き ＝ 板の幅×枚数 ＋ すき間×（枚数−1）

89×3 ＋ 5×2 ＝ 277mm → 根太の長さを277mmにする

先に板とすき間の寸法から全体を決めると、板を細く割かずに済みます。


根太の間隔

間隔 ＝（幅 − 根太の厚み）÷ 2


（600 − 38）÷ 2 ＝ 約281mm（中心から中心）

図面


単位はmm

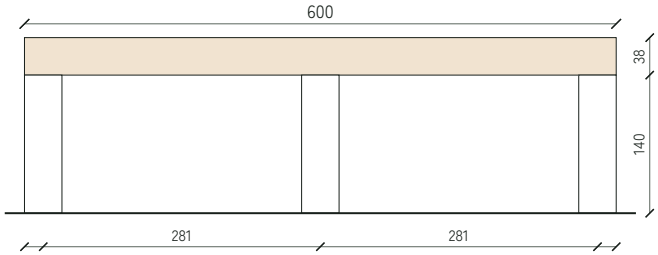


正面図（前から見た図）

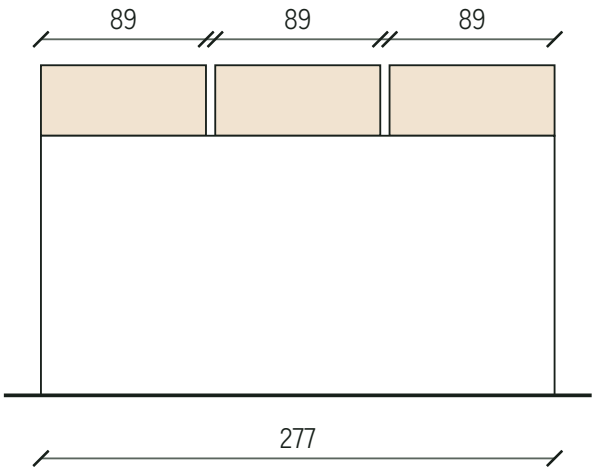

側面図（横から見た図）

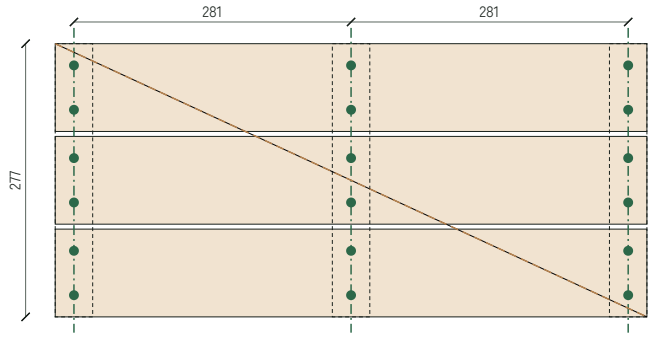

平面図　緑の線＝根太の中心線（ビスを打つ線）、●＝ビス

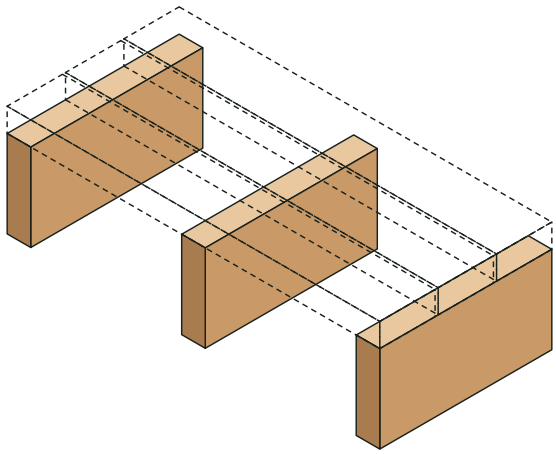

床板の下の根太（床板は破線）

部品

根太	2×6材（縦に立てる）	277mm × 3本
床板	2×4材（寝かせる）	600mm × 3枚

ビスの位置


床板1枚につき、根太1本あたり2本。板の縁から22mm内側、根太の中心線の上。合計18本。

カット表

斜線は余り

2×6材（STEP1の余り 約914mm）

914 **×1本**

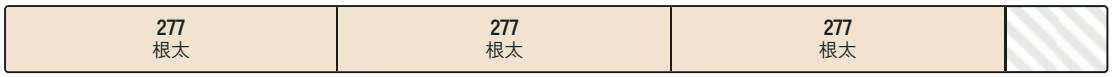

余り 約77mm

2×4材 1,820mm × 1本

1,820 **×1本**



1,820mmから600mmを3本とると余りはほぼ0。最初に端を切りそろえるときは、2〜3mmだけにする。

STEP1のおさらい

- ☐ さしがねで直角の線を引き、側面にも回す
- ☐ 線の外側（捨てる側）を切る
- ☐ 1本切るごとに次の印をつける

今回のポイント


- ☐ 根太3本は高さ（140mm）がそろっているか、立てて並べて確かめる
- ☐ 床板3枚は長さがそろうように、重ねて端を確かめる

組み立て

根太 → 1枚目 → 直角 → 残り

1 根太を並べる


1. 平らな床に根太3本を立てて並べる
2. 両端の根太の外側を600mmに、真ん中の根太を中央（両端から約281mm）に置く
3. 根太の上の面に、中心線を鉛筆で引いておく（ビスを打つ線になる）

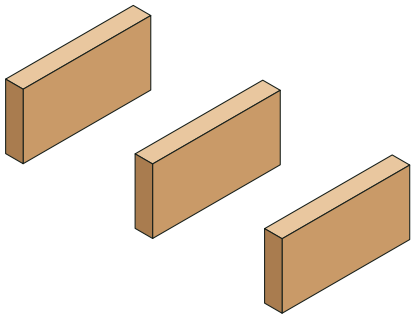

根太3本

2 1枚目を張って、直角を確かめる

1. 1枚目の床板を、根太の手前の端にそろえてのせる
2. 両端の根太に1本ずつ、下穴をあけて仮留めする
3. 3枚とも並べてから、全体の対角線を2本測る。どちらも約661mmなら直角
4. 直角が出たら、1枚目を全部の根太にビス2本ずつで留める

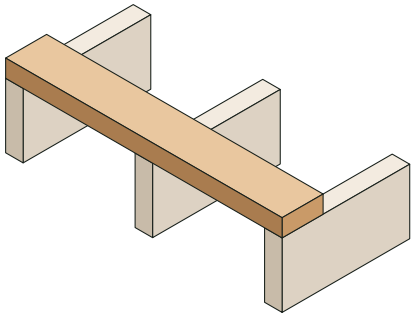


手前の1枚目から

3 すき間ゲージで残りを張る

1. 1枚目との間にすき間ゲージを2か所はさみ、2枚目を押しつけて留める
2. 3枚目も同じように張る。最後の板の外側が根太の端とそろえば正解
3. まっすぐな定規を根太の中心線に合わせて床板の上にも線を引き、その線の上にビスを打つ


ずれたときは、ビスを抜いてやり直せばよい。デッキの床板でも同じ直し方をする。

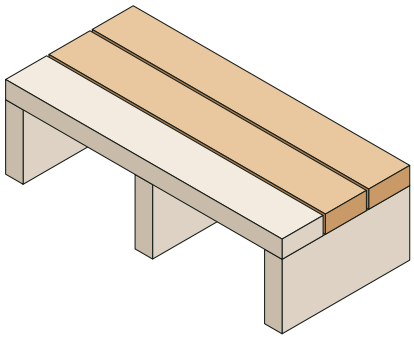

すき間5mmで2枚目・3枚目

4 仕上げる

1. 床板の角と縁をサンドペーパーで丸める
2. 屋外用の塗料を2回塗る。根太の下の木口（地面に触れる面）は特にしっかり
3. 鉢を置き、水やりの水がすき間から抜けるか確かめる

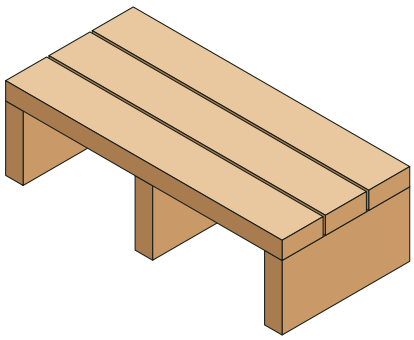

完成

できあがりチェック

全部できたらSTEP2修了

- ☐ すき間が2か所とも、端から端まで5mmでそろっている
- ☐ ビスの頭が、根太の中心線の上に一直線に並んでいる
- ☐ 対角線の2本が同じ長さ（差が3mm以内）
- ☐ 平らな床で、がたつかない
- ☐ 鉢を置いても、床板がたわまない

うまくいかなかったときは

すき間が広がっていく	床板が少し曲がっている。ゲージを両端と中央の3か所にはさみ、板を押しつけながら留める
ビスが曲がって並ぶ	線を引かずに打った。床板の上に、根太の中心線を写してから打つ
最後の板がはみ出す	すき間が5mmより広い。ゲージの厚みを確かめて張り直す

> **ウッドデッキでは：**床板が20枚以上になると、すき間のずれが積み重なります。STEP2の「ゲージをはさむ」「線を引いてから打つ」が、そのままデッキの仕上がりを決めます。

STEP1
踏み台
切る・留める

STEP2
プランター台
板を張る

STEP3
囲炉裏テーブル
枠を組む

STEP4
木製門扉
柱を建てる

卒業制作
ウッドデッキ
すべてを使う

次は STEP3「囲炉裏テーブル」

脚と枠を組み、天板の真ん中に炉をつくります。炭火を使う本格派と、飾り炉・カセットコンロ用の手軽なタイプから選べます。ウッドデッキの骨組み（大引・根太）を組む練習になります。

サイト：**ryuphoenix.com**